

[illegible]

AVR	-	AUTOMATIC VOLTAGE REGULATOR	MAG	-	MAGNETO
BA_	-	BRUSH ASSEMBLY	NEU	-	NEUTRAL
BCH	-	BATTERY CHARGER	P_	-	VSCF AVR CONNECTIONS
CB	-	CIRCUIT BREAKER	PS	-	POWER SUPPLY
CT_	-	CURRENT TRANSFORMER	R	-	RESISTOR
DPE	-	DISPLACED PHASE EXCITATION	RTR	-	ROTOR
FAN1	-	AC FAN	SC	-	STARTER CONTACTOR
FAN2	-	DC FAN	SCR	-	STARTER CONTROL RELAY
FS	-	FUEL SOLENOID	SHLD	-	SHIELD
GND	-	GROUND	SM	-	STARTER MOTOR
HOT	-	HIGH OIL TEMPERATURE SWITCH	SP_	-	SPARK PLUG
IM_	-	IGNITION MODULE	STR	-	STATOR
J_	-	MAIN CONTROLLER CONNECTIONS	TB_	-	TERMINAL BLOCK
LED	-	LED BOARD			
LOP	-	LOW OIL PRESSURE SWITCH			

12 ← **AWG SIZE**



Diagram illustrating a splice with a splice number and wire splice label. A horizontal line represents the wire, with a black rectangular splice in the center. The number '2' is written above the splice, with a line pointing to it from the label 'SPLICE NUMBER'. Below the splice, the text 'WIRE SPLICE' is written with a line pointing to the splice.

PAGE 2 OF 8 |

06/13/16	0001966-A	RELEASED FOR PRODUCTION
12/07/17	0005788-B	CHASSIS GND AWG 6 (WAS 9)


ING - DIAGRAM


STR	22	8	22	8	22	— NEU
STR	33	8	33	8	33	— NEU
STR	11	8	11	8	11	— CB
STR	44	8	44	8	44	— CB

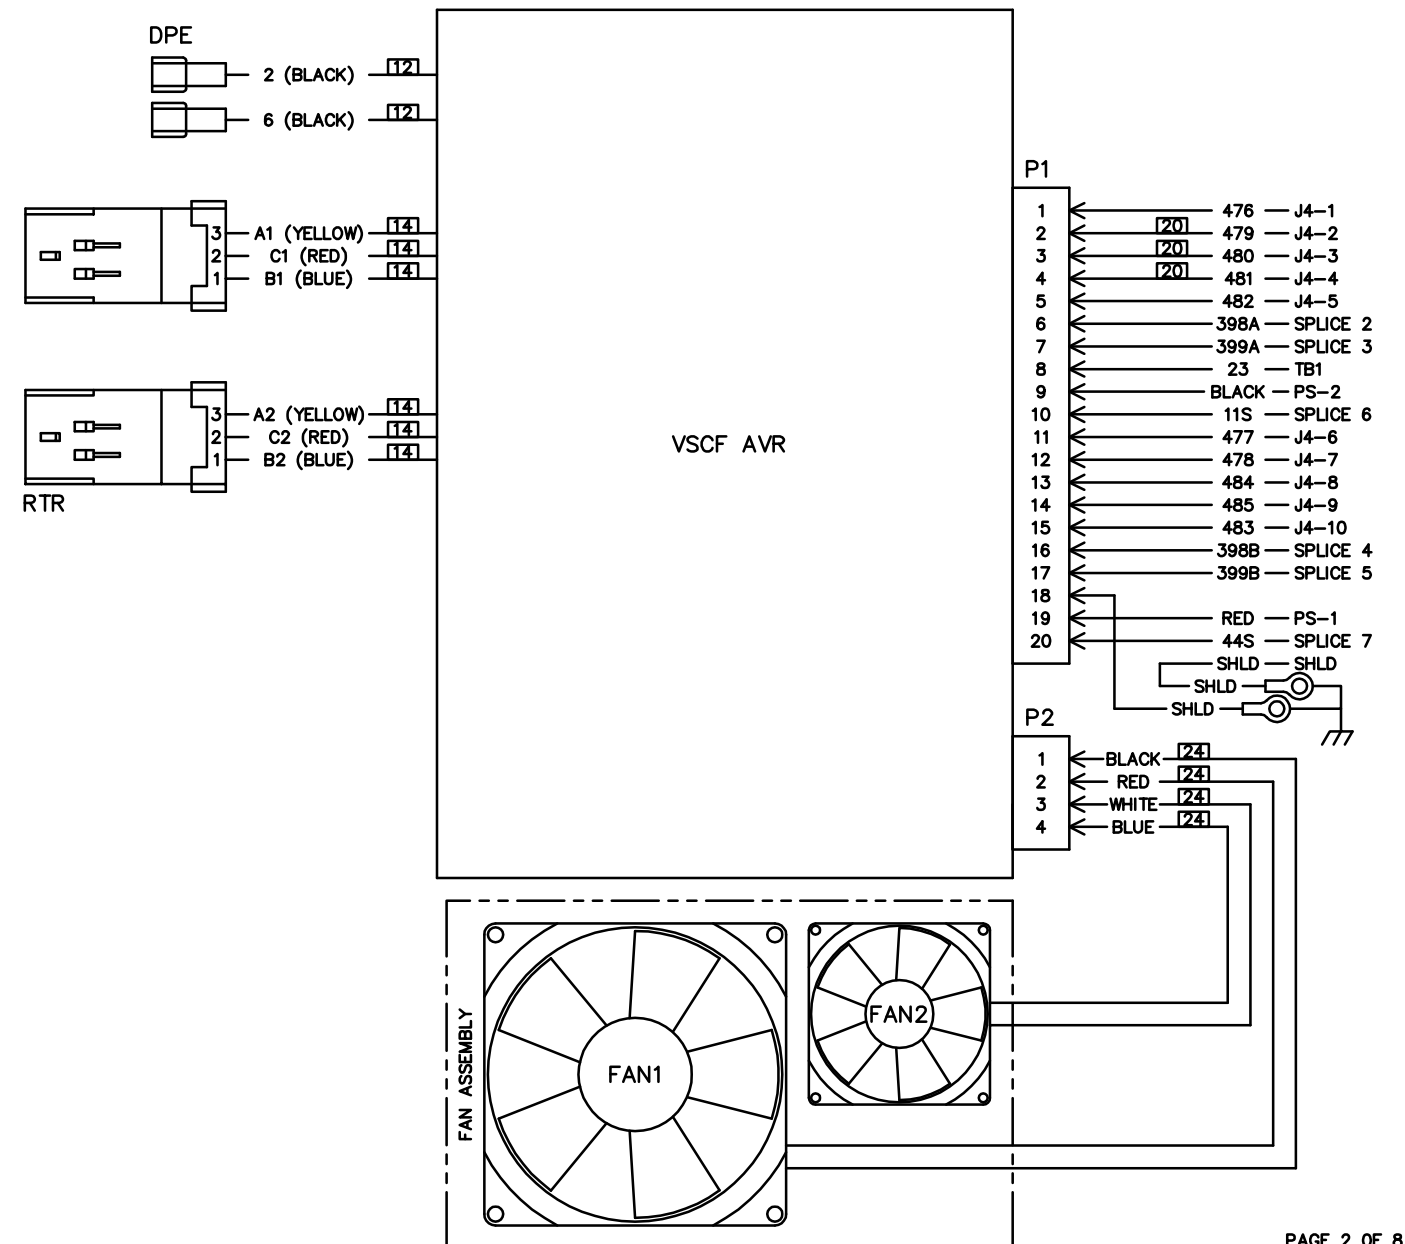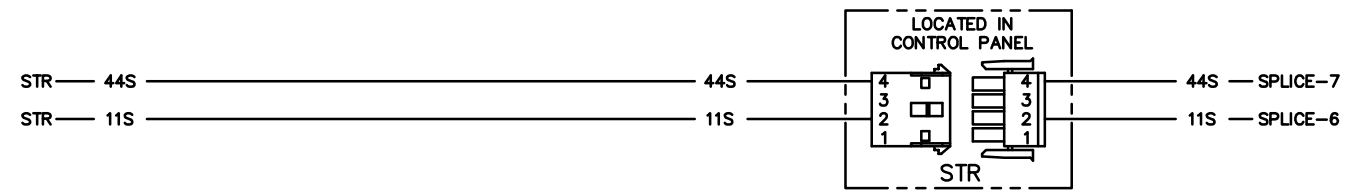


PAGE 2 OF 8 |

EST. VT.	DRAWING TITLE WIRING DIAGRAM AC HSB 20KW SYNERGY				
FINAL VT.					
DO NOT SCALE		MATERIAL	FILE NAME	0L6825.DWG	SIZE D
ALL DIMENSIONS AND TOLERANCES PER ASME Y14.5-1994			SCALE	NTS	FIRST USE
UNLESS OTHERWISE SPECIFIED 1		GENERAL NOTES: CUSTOMER SHALL BE RESPONSIBLE FOR THE ACCURACY OF THIS DRAWING WHICH IS SUPPLIED ON AN "AS-BUILT" BASIS. THE CUSTOMER SHALL BE RESPONSIBLE FOR THE ACCURACY OF THE INFORMATION PROVIDED TO THE ENGINEER. THE ENGINEER SHALL BE RESPONSIBLE FOR THE ACCURACY OF THE INFORMATION PROVIDED TO THE CUSTOMER. THE ENGINEER SHALL BE RESPONSIBLE FOR THE ACCURACY OF THE INFORMATION PROVIDED TO THE CUSTOMER.	DWG NO.	0L6825	REV
ALL DIMENSIONS UNLESS OTHERWISE SPECIFIED 1	DRAWN BY: CGF		DATE	06/01/16	B
ALL DIMENSIONS UNLESS OTHERWISE SPECIFIED 1	ALL DRAWINGS ELECTRONICALLY STORED INSIDE WINCHILL				
ALL DIMENSIONS UNLESS OTHERWISE SPECIFIED 1					

 


 

	A	B	C	D	E
1	—	—	—	—	

 

SCHEMATIC – DIAGRAM

 

EST. VT.	DRAWING TITLE WIRING DIAGRAM AC HSB 20KW SYNERGY	GENERAC[®]			
FINAL VT.					
DO NOT SCALE	MATERIAL	FILE NAME	0L6825.DWG	SIZE	D
ALL DIMENSIONS AND TOLERANCES PER ASME Y14.5-1994		SCALE	NTS	FIRST USE	G007040-0
UNLESS OTHERWISE SPECIFIED:	GENERAC PAPER SYSTEMS HAS THE OPTION OF THIS DRAWING BEING IN GENERAC'S STANDARD PAPER SYSTEM OR IN THE PAPER SYSTEM OF YOUR CHOICE. IF IT IS SUPPLIED UNDER THE OPTION OF YOUR CHOICE, THE DRAWING WILL BE SUPPLIED UNDER THE OPTION OF YOUR CHOICE.	DWG NO.	REV		
ALL DIMENSIONS IN INCHES ALL ANGLES IN DEGREES	DRAWN BY: CGF DATE 06/01/16	0L6825		B	
	ALL APPROVALS ELECTRONICALLY STORED INSIDE VINDICILL				